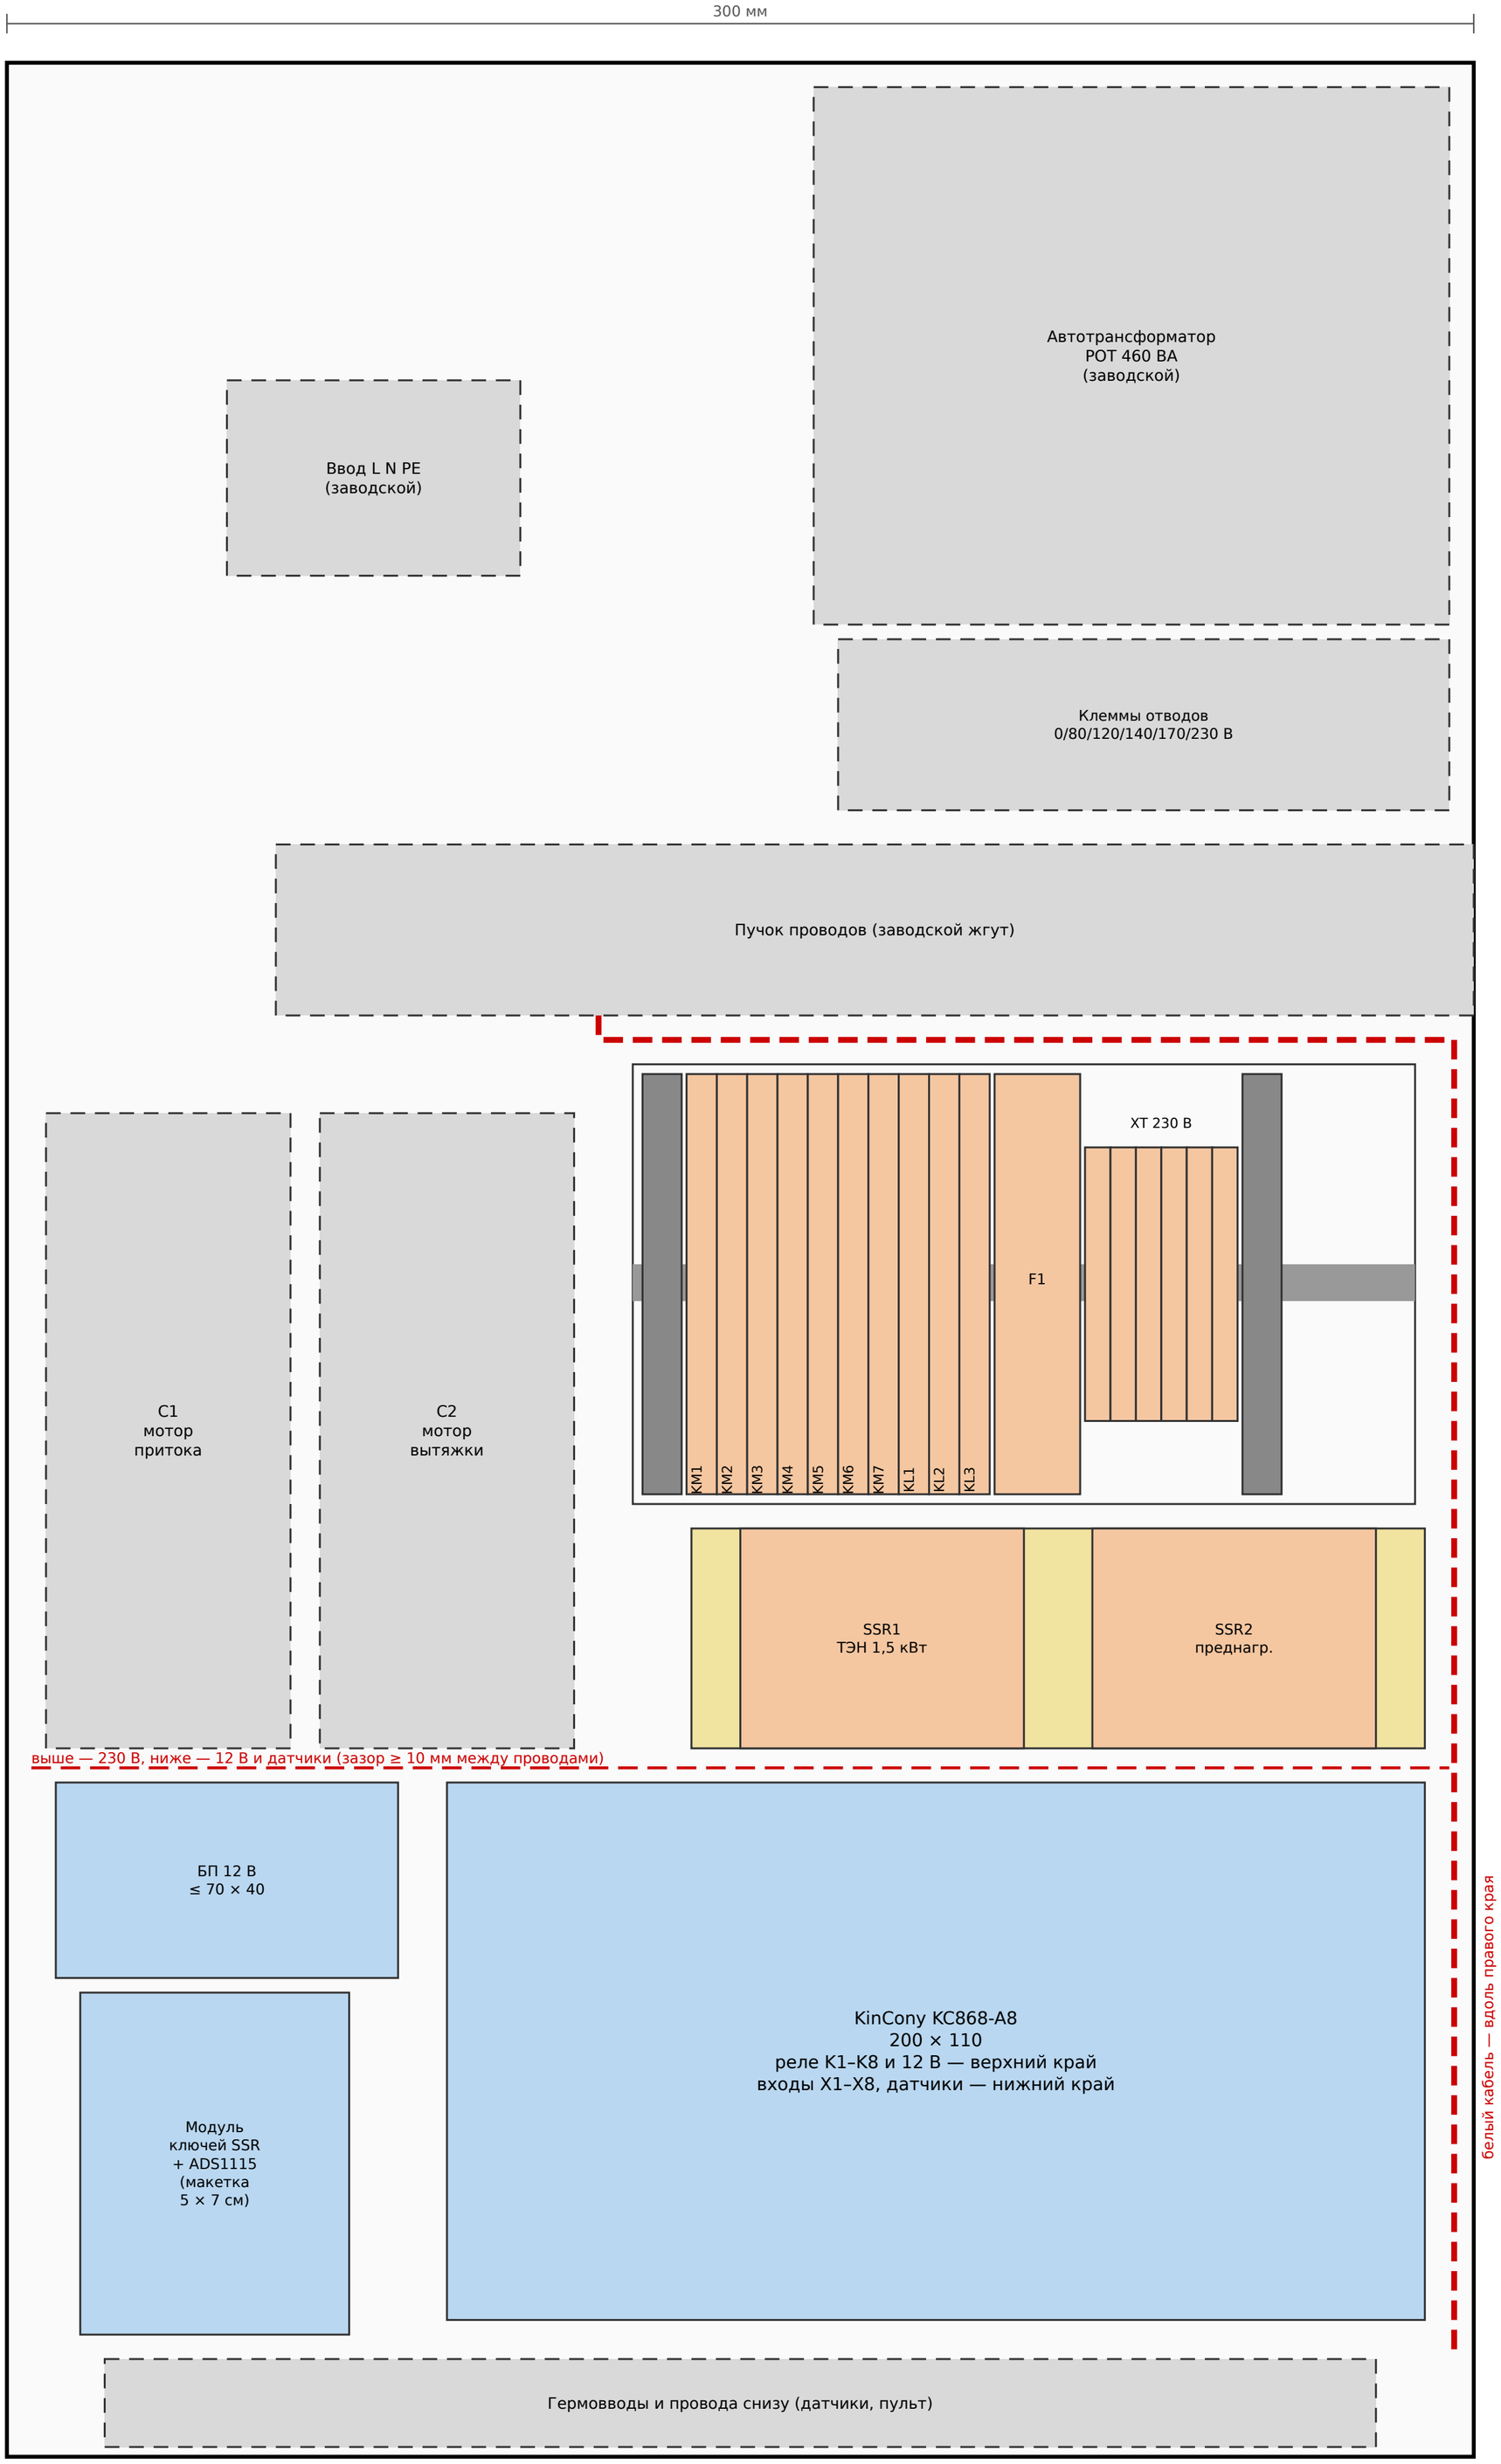


## Раскладка отсека, 1:1

- заводское — не трогаем (по фото, ±10 мм)
- новое, 230 В
- алюминий 3 мм под SSR (теплоотвод), термопаста
- новое, 12 В и датчики

Глубина отсека 100 мм: всё ниже 90 мм (рейка 7,5 + реле ≤ 82; SSR плоские).

KM1–KM3 — ступени притока,
KM4–KM6 — вытяжки: узкие реле 6,2 мм, CO, катушка 12 В DC; переключают отвод автотрансформатора на мотор, блокировка NC-контактами (docs/salda_in_unit.md).
KM7 — заслонка. KL1–KL3 — контроль термостатов (катушка 230 В).
F1 — предохранитель БП 12 В (0,5 А).
XT 230 В — N и PE моторов, заслонки.

SSR лежат на алюминиевой полосе: силовые клеммы вверх (к 230 В), клеммы управления вниз (к ключам).

Белый кабель (заводской) освобождает место под плату — переложить к правому краю.

Ввод, автотрансформатор, конденсаторы, жгут — на своих местах, как с завода.

Сверить по месту: координаты заводских узлов сняты с фото (±10 мм).